



一、有一配置預力(prestressed)暨非預力(nonprestressed)鋼絞線之梁斷面如圖 1 所示，試回答下列問題。(20 分)

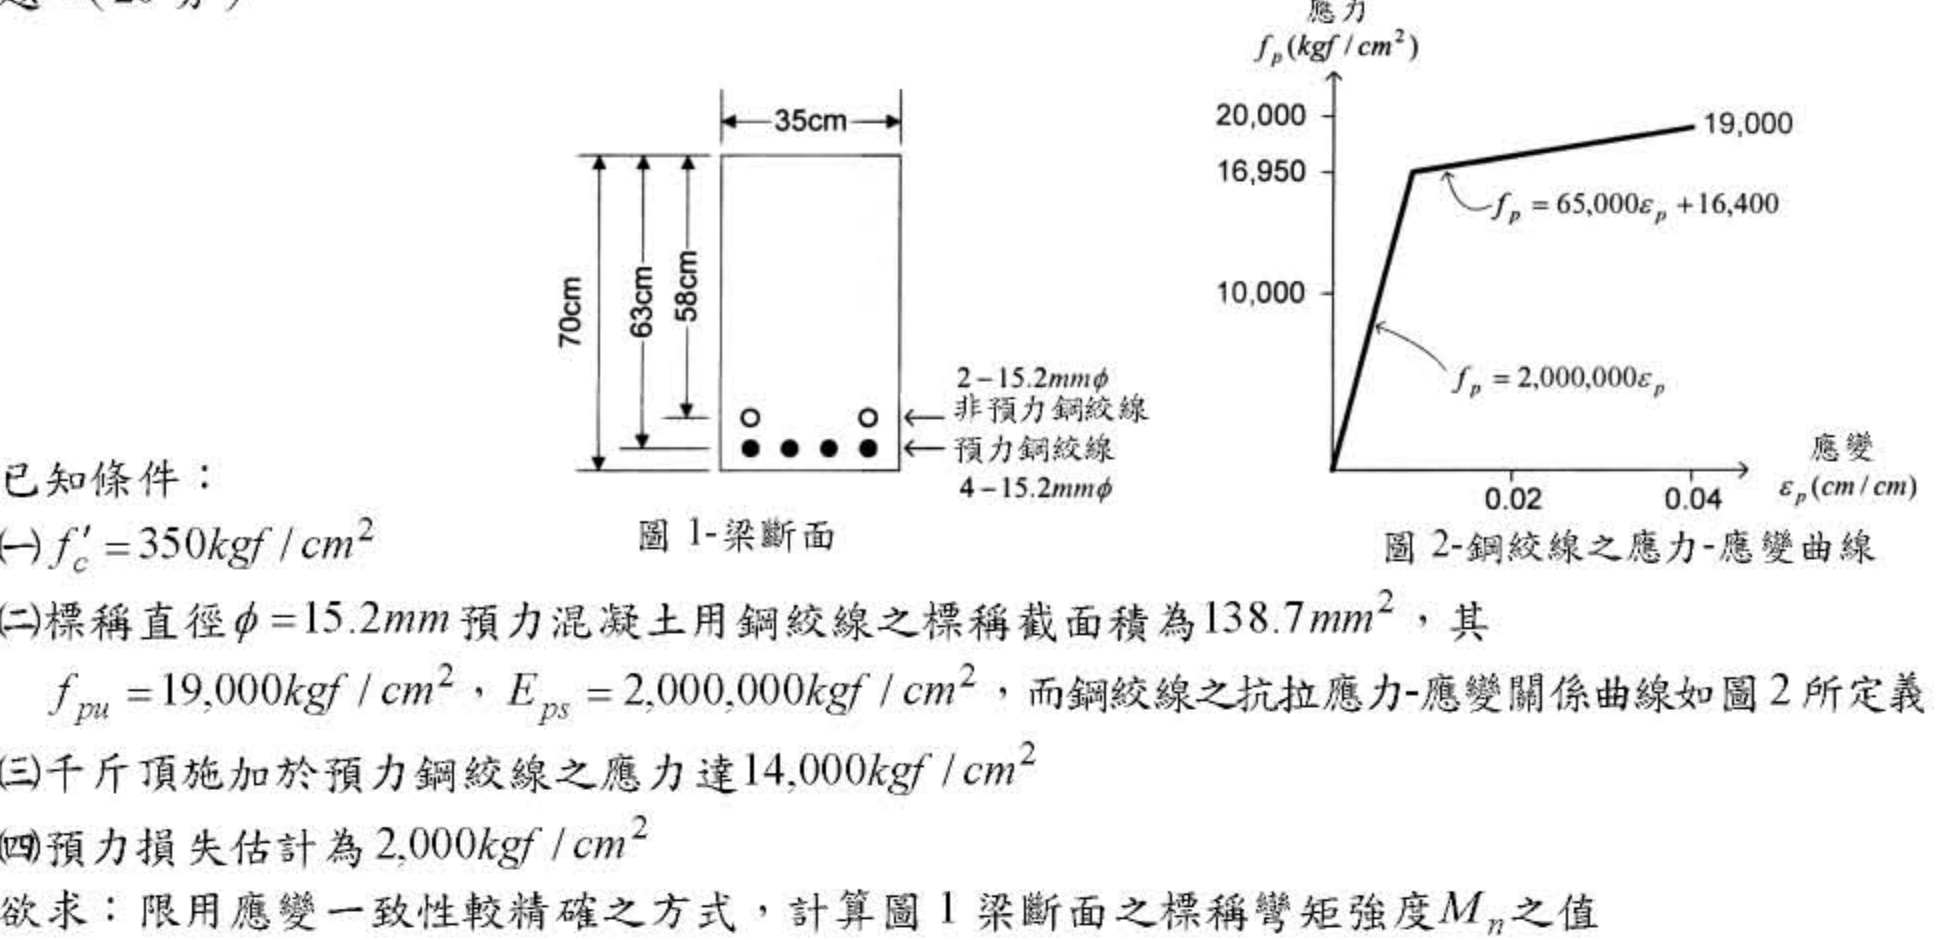


二、有一耐震鋼筋混凝土柱之立面及斷面情況如圖 3 所示，若欲執行柱主筋之搭接設計，試按民國 92 年 1 月 1 日生效，由營建雜誌社發行之「結構混凝土設計規範」設計之。(20 分)

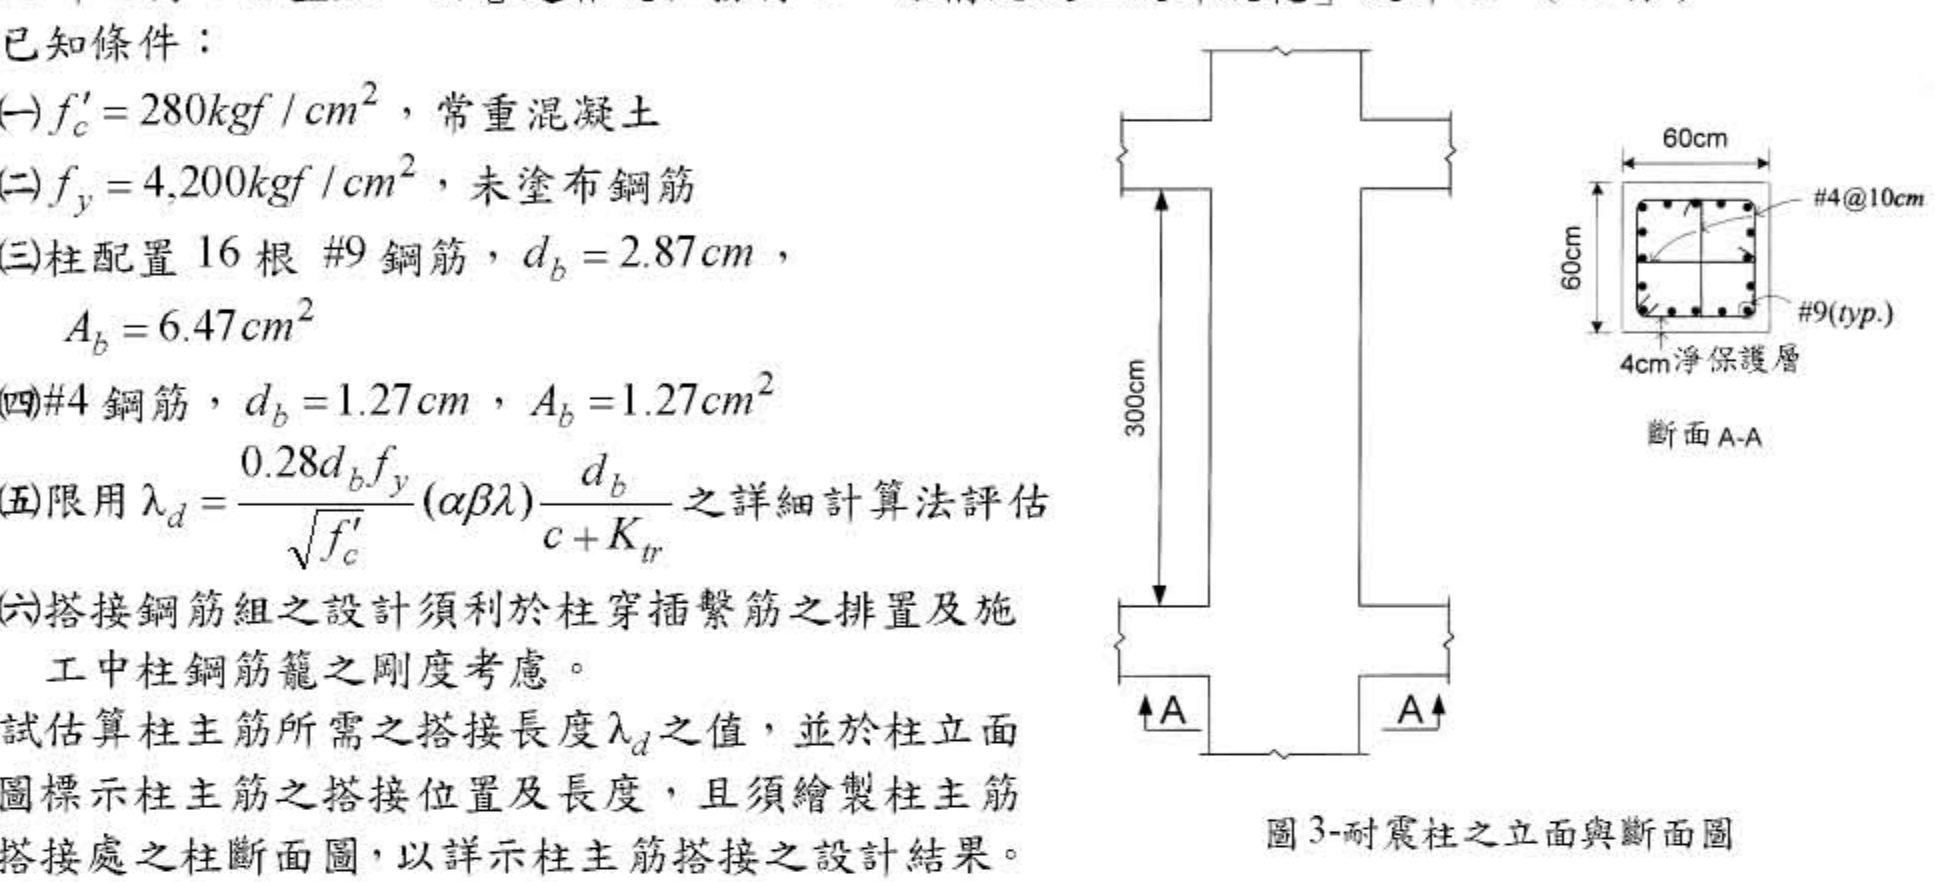

(請接背面)

三、有一耐震鋼筋混凝土中間層內跨之梁柱接頭組件如圖 4 所示，試按民國 92 年 1 月 1 日生效，由營建雜誌社發行之「結構混凝土設計規範」設計之。(20 分)

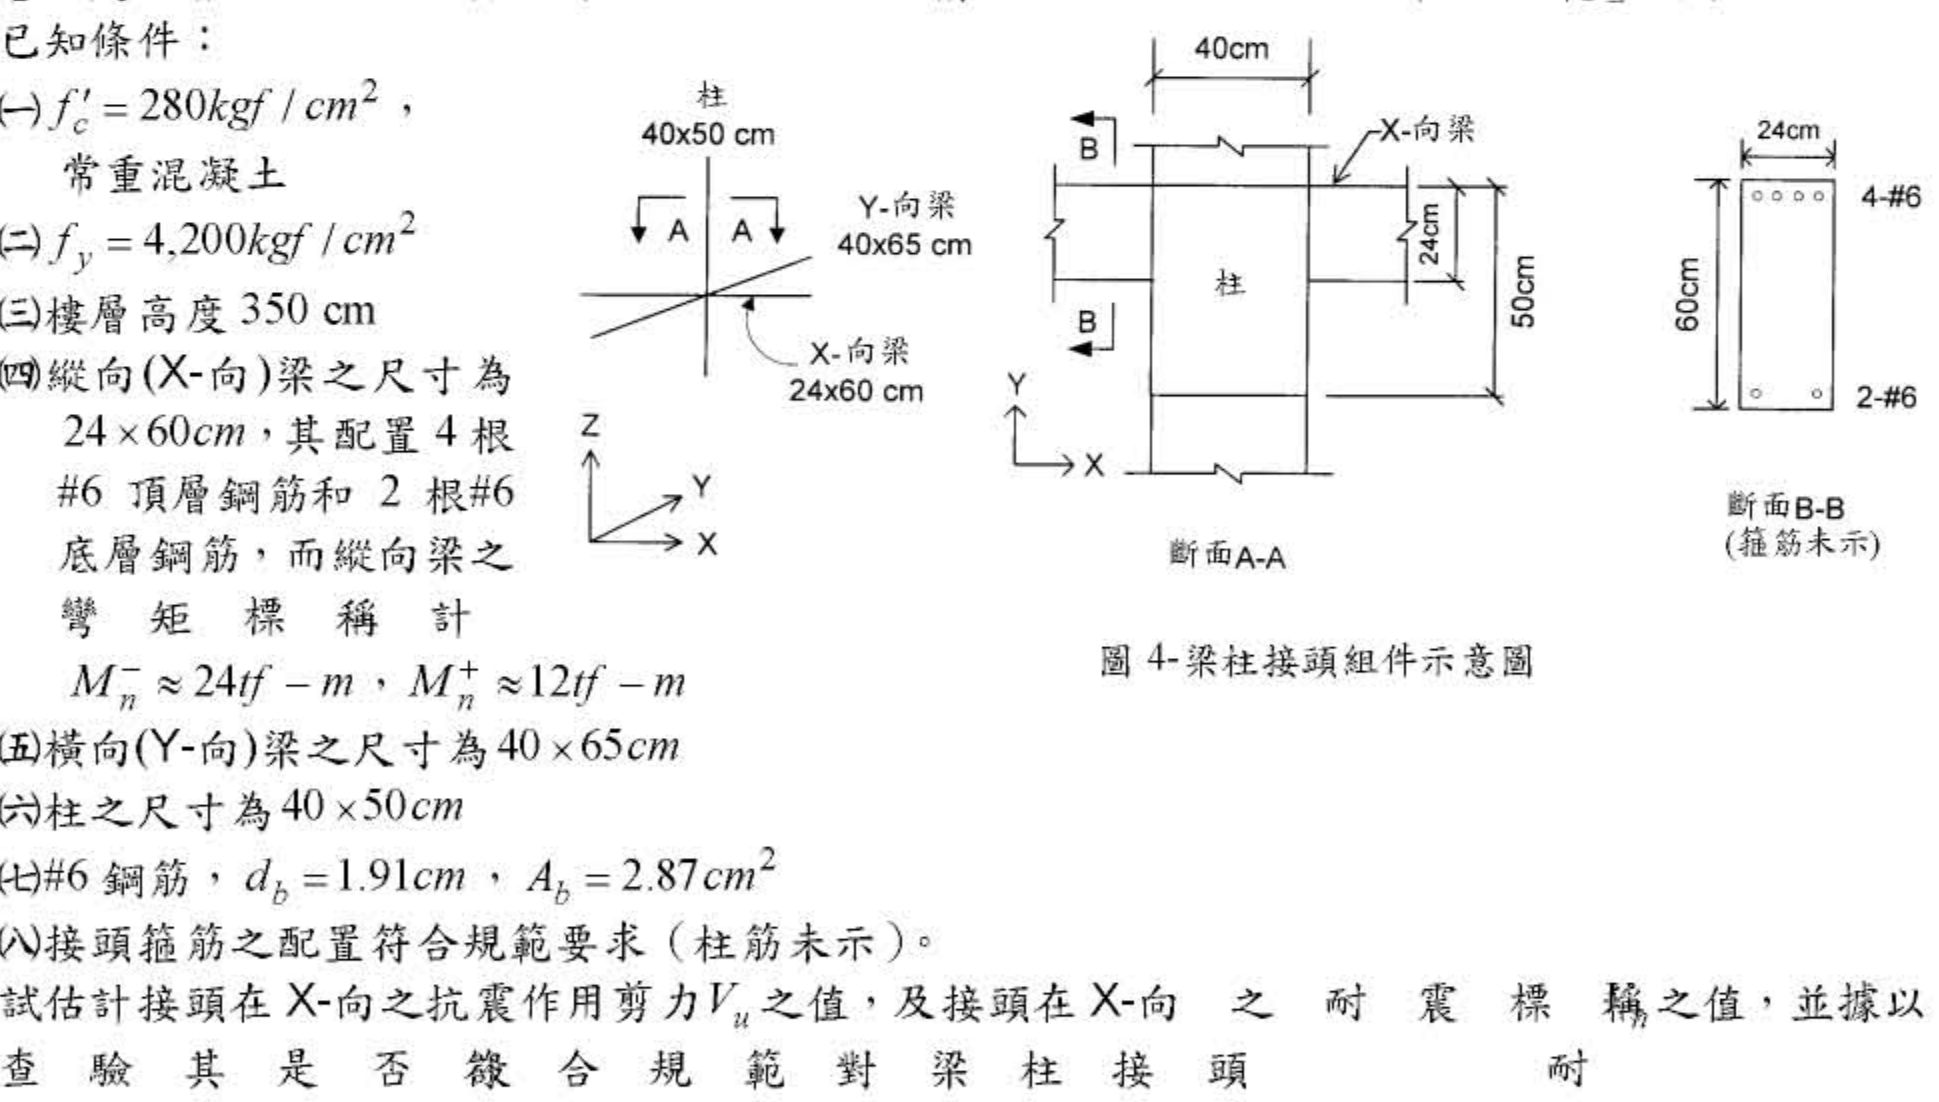

四、有一兩層樓高作耐震用之鋼筋混凝土剪力牆如圖 5 所示，試按民國 92 年 1 月 1 日生效，由營建雜誌社發行之「結構混凝土設計規範」來設計剪力牆之鋼筋配置。(40 分)

